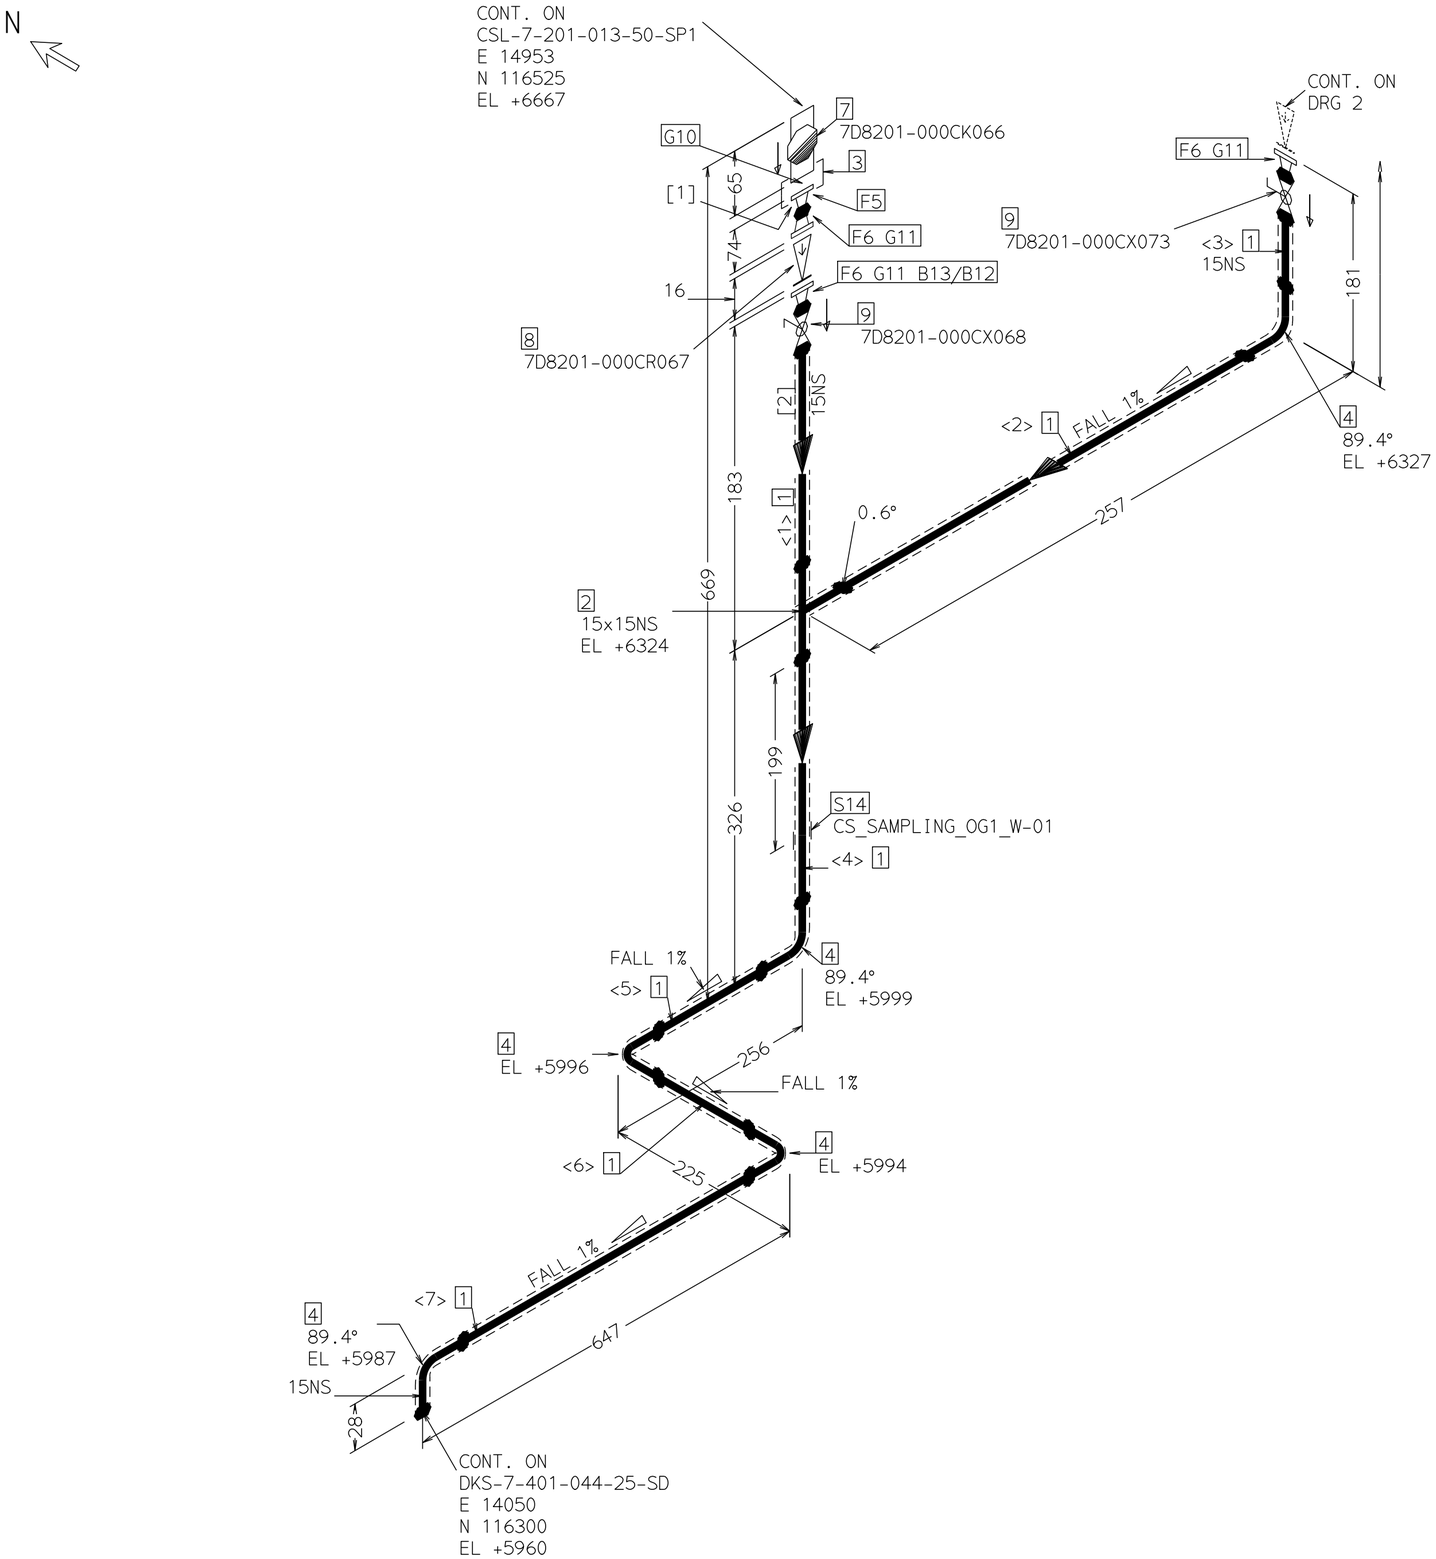

Construction and connection dimensions must be checked on site!
All axis and positions must be checked on site!

FABRICATION MATERIALS

PT NO	COMPONENT DESCRIPTION	N.S. (MM)	ITEM CODE	QTY
	PIPE			
1	Pipe DIN EN ISO 1127 acc.to Pipespec	15	SD/PPA16331-P100_015	1.6M
	FITTINGS			
2	Tee - type A - type long - DIN EN 10253-4 acc.to Pipespec	15 x 15	SD/ETAN6331-P1L0_015-015	1
3	Clamp with anti-tipping device for TC acc.to Pipespec	15	SD/BKF26001-S000_015	1
4	Elbow 90° - type A - design 3D (r=ca.1,5Da) - DIN EN 10253-4 acc.to Pipespec	15	SD/EBAN6331-P100_015	5
	FLANGES			
5	Clamp connection - flat sealing surface - DIN 32676 series B, TC50.5mm acc.to Pipespec	15	SD/FKF16331-0B41_015	1
6	Welding neck flange - type 11 - Type B1 - DIN EN 1092-1 PN 40 acc.to Pipespec	15	SD/FVB16331-1150_015	3
	VALVES / IN-LINE ITEMS			
7	Steam trap - thermal capsule - clamps DIN 32676 series B, TC 50.5mm - DN 15	15	SD/KACB640S-V02H_015	1
8	Lift check valve - wafer type - DIN EN 13709 acc.to Pipespec	15	SD/RVE2610Y-XZ30_015	1
9	Ball valve manual- welding ends -full bore acc.to Pipespec	15	SD/HKA2640M-H030_015	2

ERECTION MATERIALS

PT NO	COMPONENT DESCRIPTION	N.S. (MM)	ITEM CODE	QTY
	GASKETS			
10	TC seal-DIN 32676 Gylon 3504	15	SD/GP089611-0000_015	1
11	Flat gasket - Type IBC - DIN EN 1514-1 PN40 Gylon 3504	15	SD/GFB19611-1550_015	3
	BOLTS			
12	65 lg Hex. head bolts with nut - with shaft - DIN EN ISO 4014 M12 A2-70	12	B_ISO_4014-A2-70_M12_MACH6	4
13	Hex. nut M12 A2-70	12	B_ISO_4014-A2-70_M12_NUT	4
	SUPPORTS			
14	ASSEMBLY GROUP BG15-F80-1/2", DN 15; ARTICLE NO. 110227	15	SIK/BG15-F80-1/2-15	1
	PIPE SPOOLS			
	[1] [2]			

CUT PIPE LENGTH

ITEM CODE	PIECE NO	CUT LENGTH	N.S. (MM)	REMARKS	END PREP.
SD/PPA16331-P100_015	<1>	50	15		BE/BE
SD/PPA16331-P100_015	<2>	204	15		BE/PE
SD/PPA16331-P100_015	<3>	45	15		BE/BE
SD/PPA16331-P100_015	<4>	273	15		BE/BE
SD/PPA16331-P100_015	<5>	200	15		BE/BE
SD/PPA16331-P100_015	<6>	169	15		BE/BE
SD/PPA16331-P100_015	<7>	591	15		BE/BE

Rev.	Date	Description	Issued	Checked	Released
02	18 Jan 2024	AFC	THPR	DATL	JYEN
01	30 Nov 2023	For review	JYEN	DATL	JUCH

peleven®

ThermoFisher SCIENTIFIC

Issued for construction: Date: 18 Jan 2024 Signature:

Pipe class	Insulation	Floor
SD	H3	1
P&ID-No.	CH06822004-BD-PI-1179	

Project: 5K SUT | Project-No. Peleven | CH06823001

Isometric Number / Pipe name: DKS-7-401-023-15-SD

Page 1 / 2