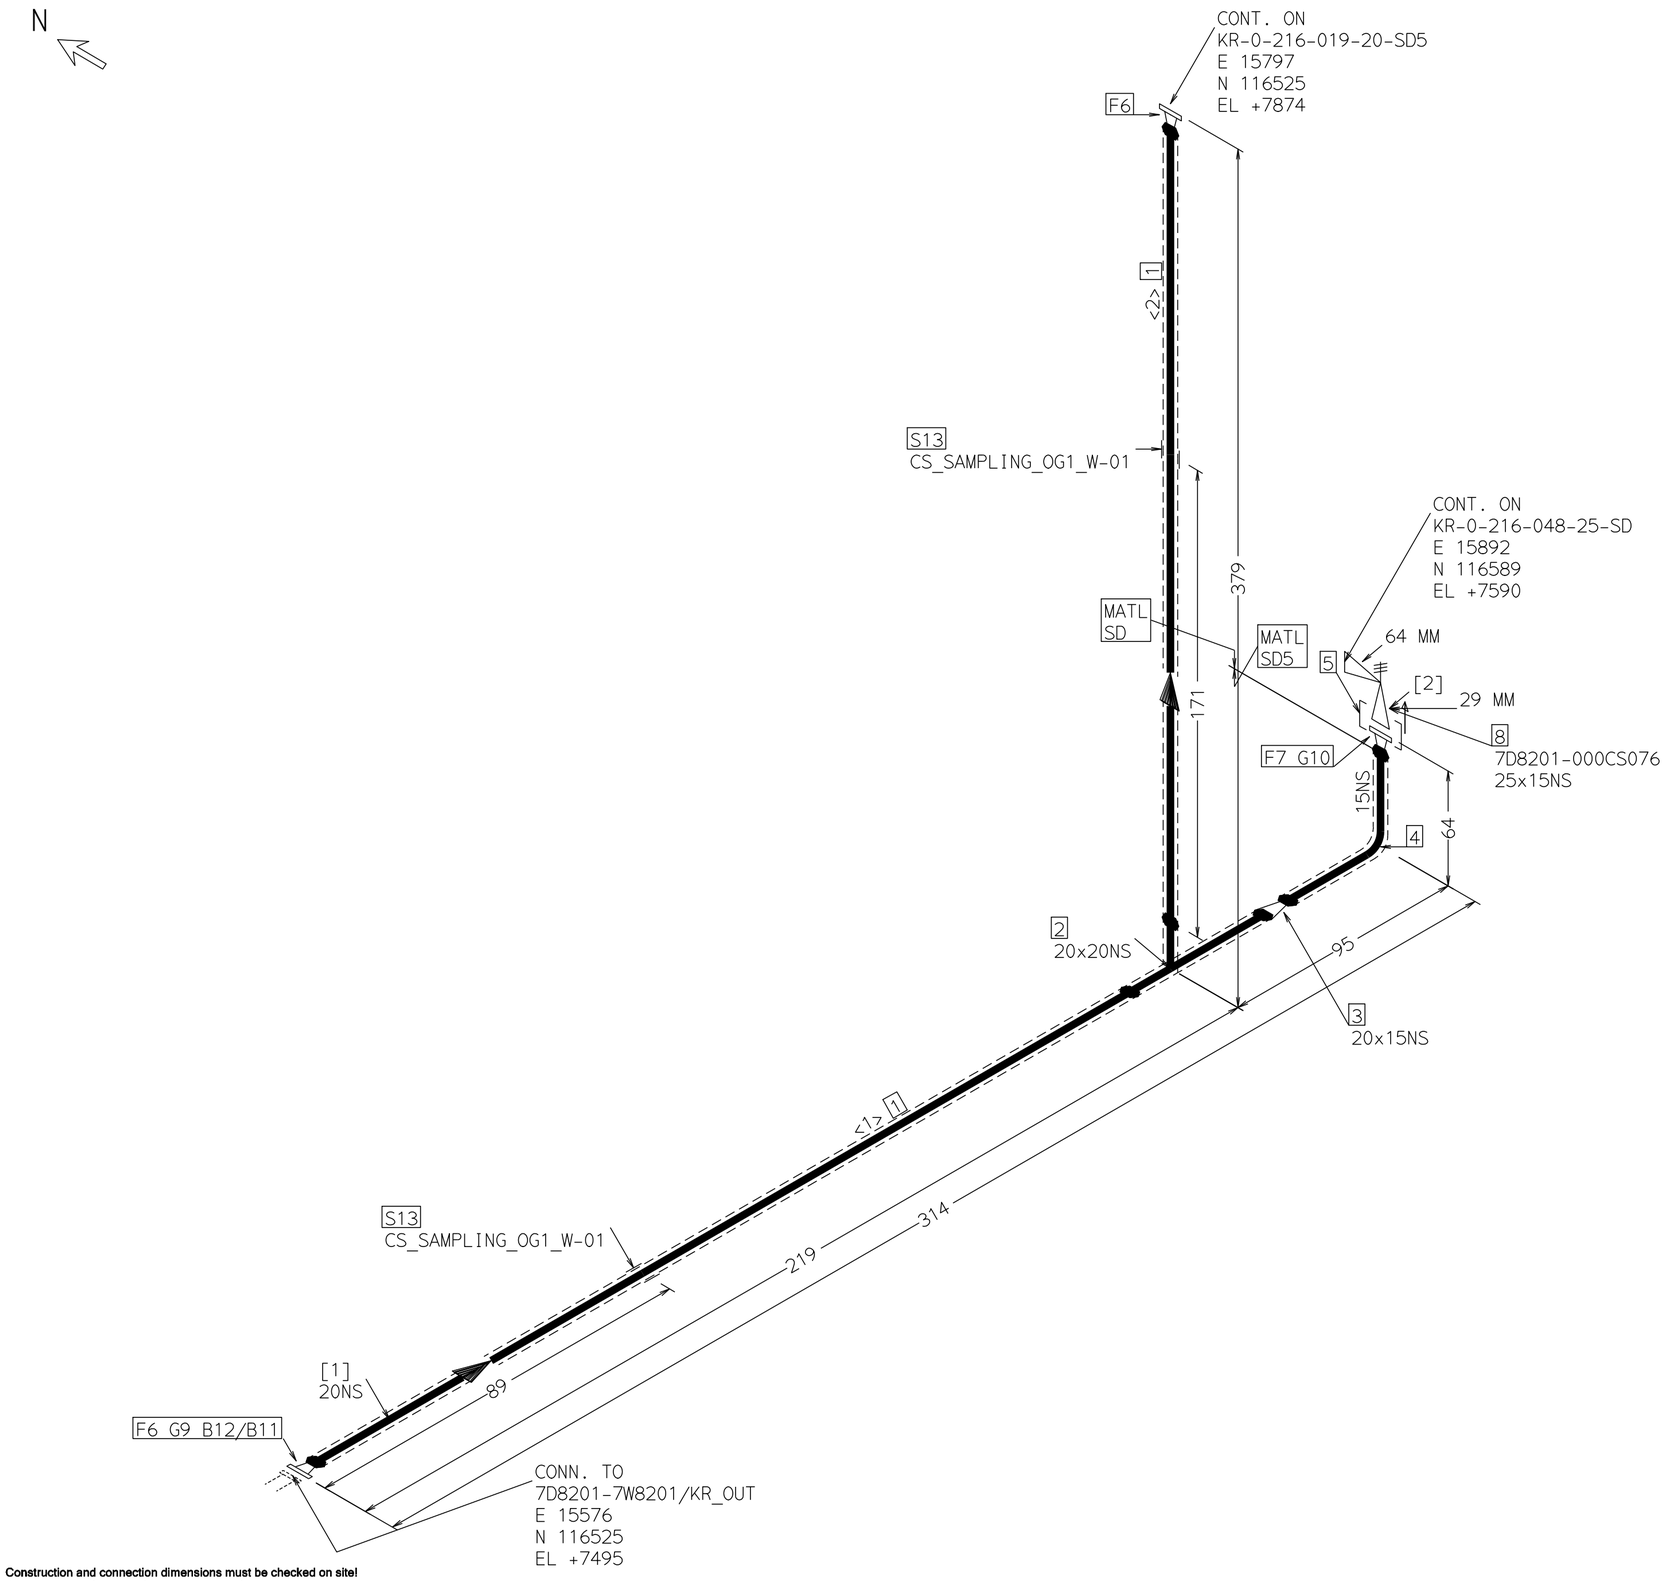

Construction and connection dimensions must be checked on site!
All axis and positions must be checked on site!

FABRICATION MATERIALS

PT NO	COMPONENT DESCRIPTION	N.S. (MM)	ITEM CODE	QTY
	PIPE			
1	Pipe DIN EN ISO 1127 acc.to Pipespec	20	SD5/PPA16331-P100_020	0.5M
	FITTINGS			
2	Tee - type A - type long - DIN EN 10253-4 acc.to Pipespec	20 x 20	SD5/ETAN6331-P1G0_020-020	1
3	Reducer - concentric acc.to Pipespec	20 x 15	SD5/EKA06331-P100_020-015	1
4	Elbow 90° - type A - design 3D (r=ca.1,5Da) - DIN EN 10253-4 acc.to Pipespec	15	SD5/EBA06331-P1A0_015	1
5	Clamp with anti-tipping device for TC acc.to Pipespec	15	SD/BKF26001-S000_015	1
	FLANGES			
6	Welding neck flange - type 11 - Type B1 - DIN EN 1092-1 PN 40 acc.to Pipespec	20	SD5/FVB16331-1150_020	2
7	Clamp connection - flat sealing surface - DIN 32676 series B, TC50.5mm acc.to Pipespec	15	SD/FKF16331-0B41_015	1
	INSTRUMENTS			
8	Safety valve TriClamp 7D8201-000CS076	25 x 15		1

ERECTION MATERIALS

PT NO	COMPONENT DESCRIPTION	N.S. (MM)	ITEM CODE	QTY
	GASKETS			
9	Flat gasket - Type IBC - DIN EN 1514-1 PN40 Klingersil C-4430	20	SD5/GFB19941-2030_020	1
10	TC seal-DIN 32676 Gylon 3504	15	SD/GP089611-0000_015	1
	BOLTS			
11	50 lg Hex. head bolts with nut - with shaft - DIN EN ISO 4014 M12 A2-70	12	B_ISO_4014-A2-70_M12_MACH5	4
12	Hex. nut M12 A2-70	12	B_ISO_4014-A2-70_M12_NUT	4
	SUPPORTS			
13	ASSEMBLY GROUP BG45-F80-1/2", DN20; ARTICLE NO. 110300	20	SIK/BG45-F80-1/2-20	2
	PIPE SPOOLS			
	[1] [2]			

CUT PIPE LENGTH

ITEM CODE	PIECE NO	CUT LENGTH	N.S. (MM)	REMARKS	END PREP.
SD5/PPA16331-P100_020	<1>	150	20		BE/BE
SD5/PPA16331-P100_020	<2>	310	20		BE/BE

Rev.	Date	Description	Issued	Checked	Released
02	18 Jan 2024	AFC	THPR	DATL	JYEN
01	30 Nov 2023	For review	JYEN	DATL	JUCH

peleven®

ThermoFisher SCIENTIFIC

Issued for construction: Date: 18 Jan 2024 Signature:

Pipe class	Insulation	Floor
SD5		1
P&ID-No.	CH06822004-BD-PI-1179	

Project: 5K SUT | Project-No. Peleven | CH06823001

Isometric Number / Pipe name: KR-0-216-047-20-SD5

Page 1 / 1