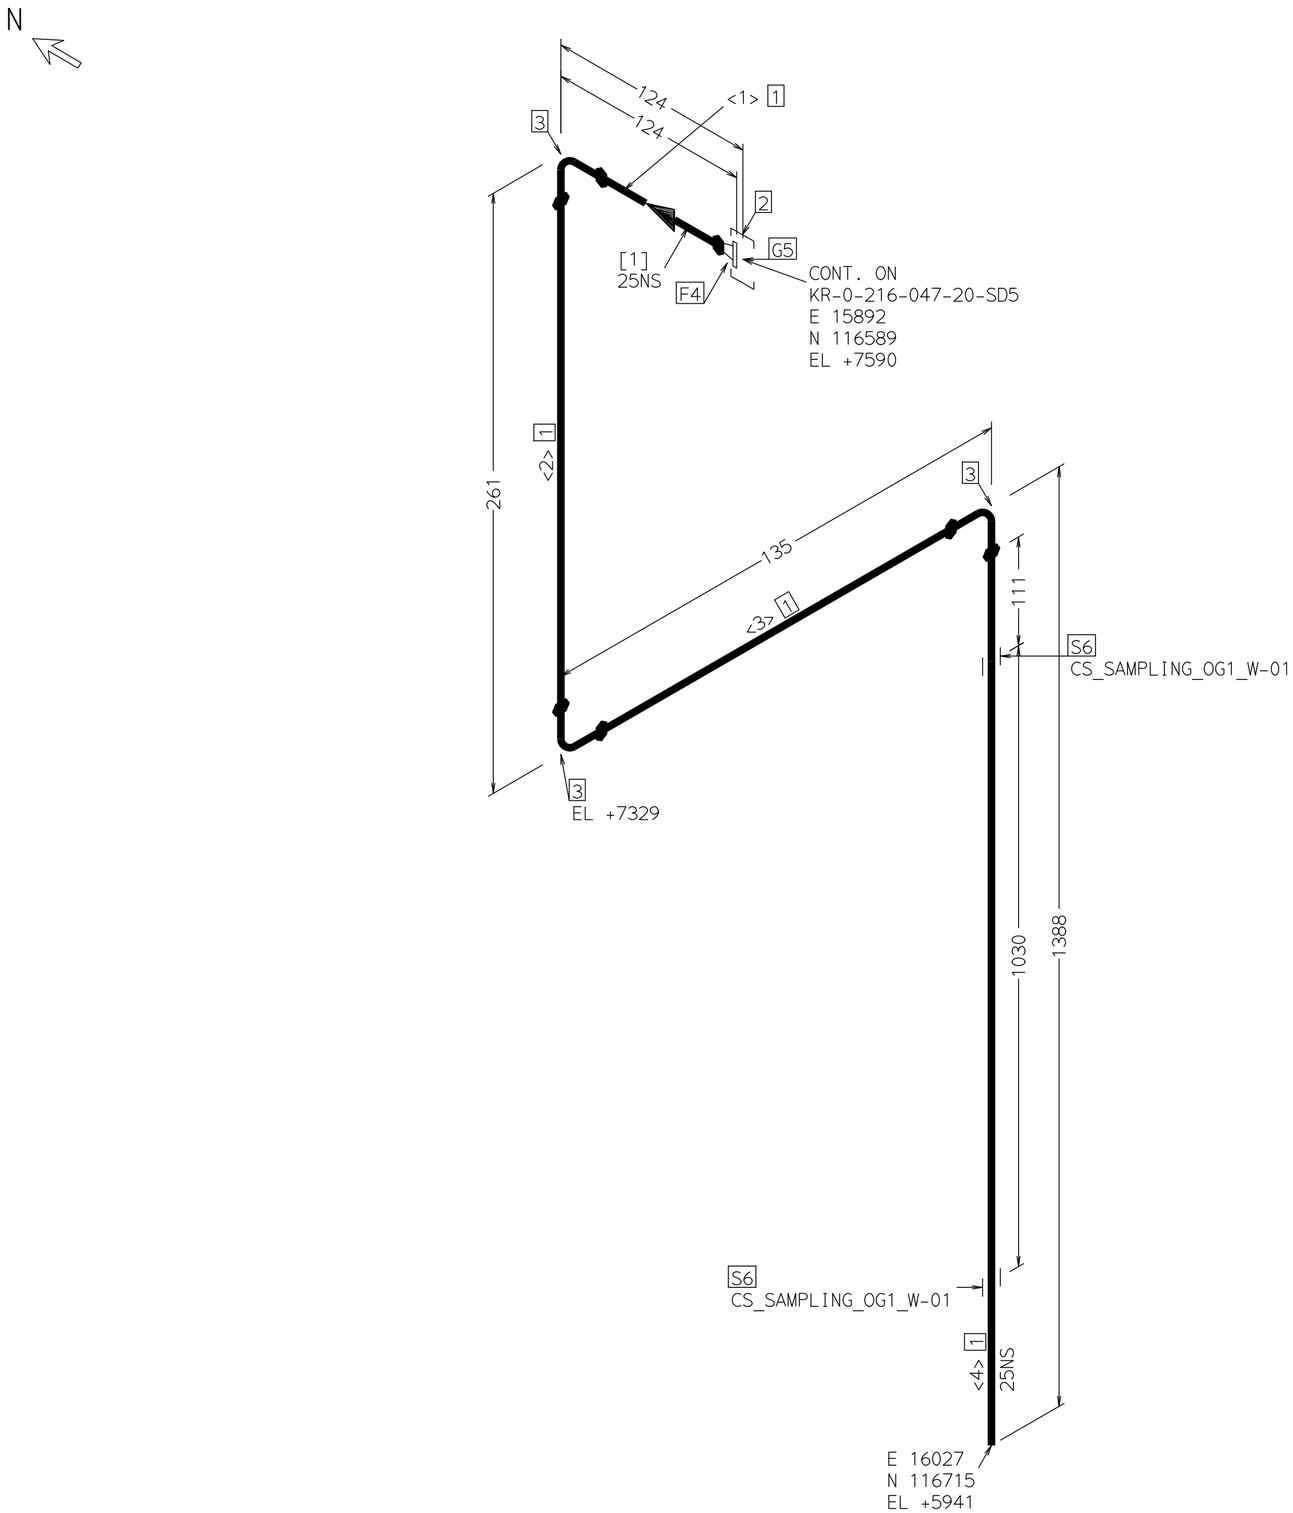

FABRICATION MATERIALS

PT NO	COMPONENT DESCRIPTION	N.S. (MM)	ITEM CODE	QTY
	PIPE			
1	Pipe DIN EN ISO 1127 acc.to Pipespec	25	SD/PPA16331-P100_025	1.7M
	FITTINGS			
2	Clamp with anti-tipping device for TC acc.to Pipespec	25	SD/BKF26001-S000_025	1
3	Elbow 90° - type A - design 3D (r=ca.1,5Da) - DIN EN 10253-4 acc.to Pipespec	25	SD/EBAN6331-P100_025	3
	FLANGES			
4	Clamp connection - flat sealing surface - DIN 32676 series B, TC50.5mm acc.to Pipespec	25	SD/FKF16331-0B41_025	1

ERECTION MATERIALS

PT NO	COMPONENT DESCRIPTION	N.S. (MM)	ITEM CODE	QTY
	GASKETS			
5	TC seal-DIN 32676 Gylon 3504	25	SD/GP089611-0000_025	1
	SUPPORTS			
6	ASSEMBLY GROUP BG15-F80-1/2", DN 25; ARTICLE NO. 110229	25	SIK/BG15-F80-1/2-25	2
	PIPE SPOOLS			
	[1]			

CUT PIPE LENGTH

ITEM CODE	PIECE NO	CUT LENGTH	N.S. (MM)	REMARKS	END PREP.
SD/PPA16331-P100_025	<1>	50	25		BE/BE
SD/PPA16331-P100_025	<2>	185	25		BE/BE
SD/PPA16331-P100_025	<3>	59	25		BE/BE
SD/PPA16331-P100_025	<4>	1350	25		BE/PE

Construction and connection dimensions must be checked on site!
All axis and positions must be checked on site!

Rev.	Date	Description	Issued	Checked	Released
02	18 Jan 2024	AFC	THPR	DATL	JYEN
01	30 Nov 2023	For review	JYEN	DATL	JUCH

peleven®

ThermoFisher SCIENTIFIC

Issued for construction: Date: 18 Jan 2024 Signature:

Pipe class	Insulation	Floor
SD		1
P&ID-No.	CH06822004-BD-PI-1179	

Project: 5K SUT | Project-No. Peleven | CH06823001

Isometric Number / Pipe name: KR-0-216-048-25-SD

Page 1 / 1