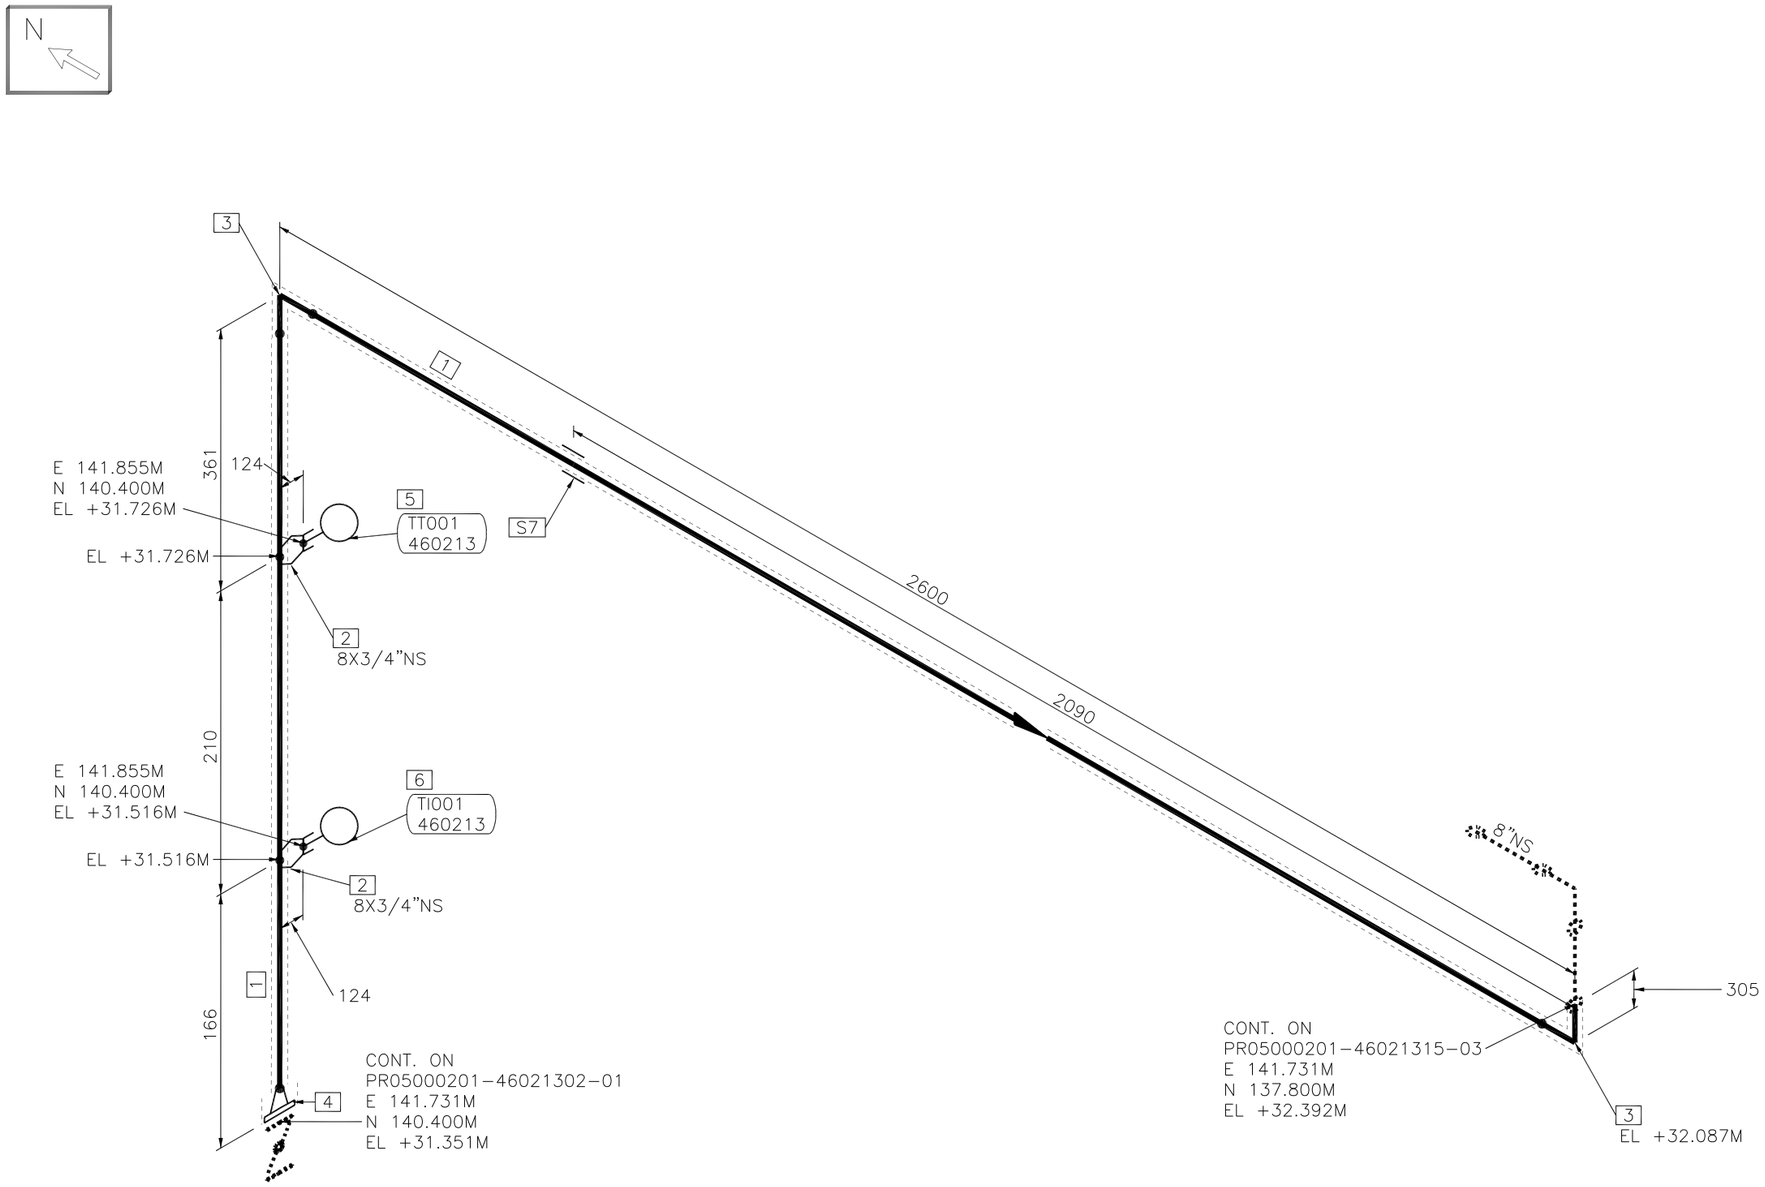

FOR ISOMETRIC NOTES PLEASE REFER TO PM DOCUMENT IE0312206-43-LI-0003

CONTRACT:	MEP2	ISSUE							
ISO CATEGORY:	CATEGORY 1	ISSUE							
SYSTEM NO.		ISSUE							
STRESS ANALYSIS	TYPE 1 EXEMPT PIPING	ISSUE							
PED CAT.	SEE PROCESS LINE LIST	ISSUE		0	ISSUE FOR CONSTRUCTION	WM	DB	PS	27 NOV 2018
P + ID	SEE PROCESS LINE LIST	ISSUE		ISSUE	DESCRIPTION	ORIG	CHK'D	PM APP	DATE

MATERIALS TAKE OFF

No.	QTY.	SIZE	DESCRIPTION	SPEC
1	2.4 M	8	PIPE CS, SMLS OR WELDED, SCH 40, ASTM A53	SP-8C
2	2	8X3/4	SOCKOLET, CS, SCH 80, ASTM A53	SP-8C
3	2	8	90 ELL. BW, WROUGHT CS, SMLS OR WELDED, SCH 40, ASTM A234	SP-8C
4	1	8	FLG WN, 150LB RF, FORGED CS, ASTM A105	SP-8C
5	1	3/4	TEMPERATURE TRANSMITTER 20MM SW THERMOWELD TT001-460213	SP-8C
6	1	3/4	TEMPERATURE INDICATOR 20MM SW THERMOWELD TI001-460213	SP-8C
7	1	12	PIPE SUPPORT, CS-05	SP-8C

PM GROUP

MSD Animal Health

CLIENT	MSD BOXMEER
PROJECT	STERILE FILLING FREEZE DRYING & CUB
LINE No.	8-WGKR-PE005-46021315-SP8C-N-CC
PROJECT No. IE0312206	DRAWING No. PR05000201-46021315-04
CLIENT REF. PE005.001	REV 0