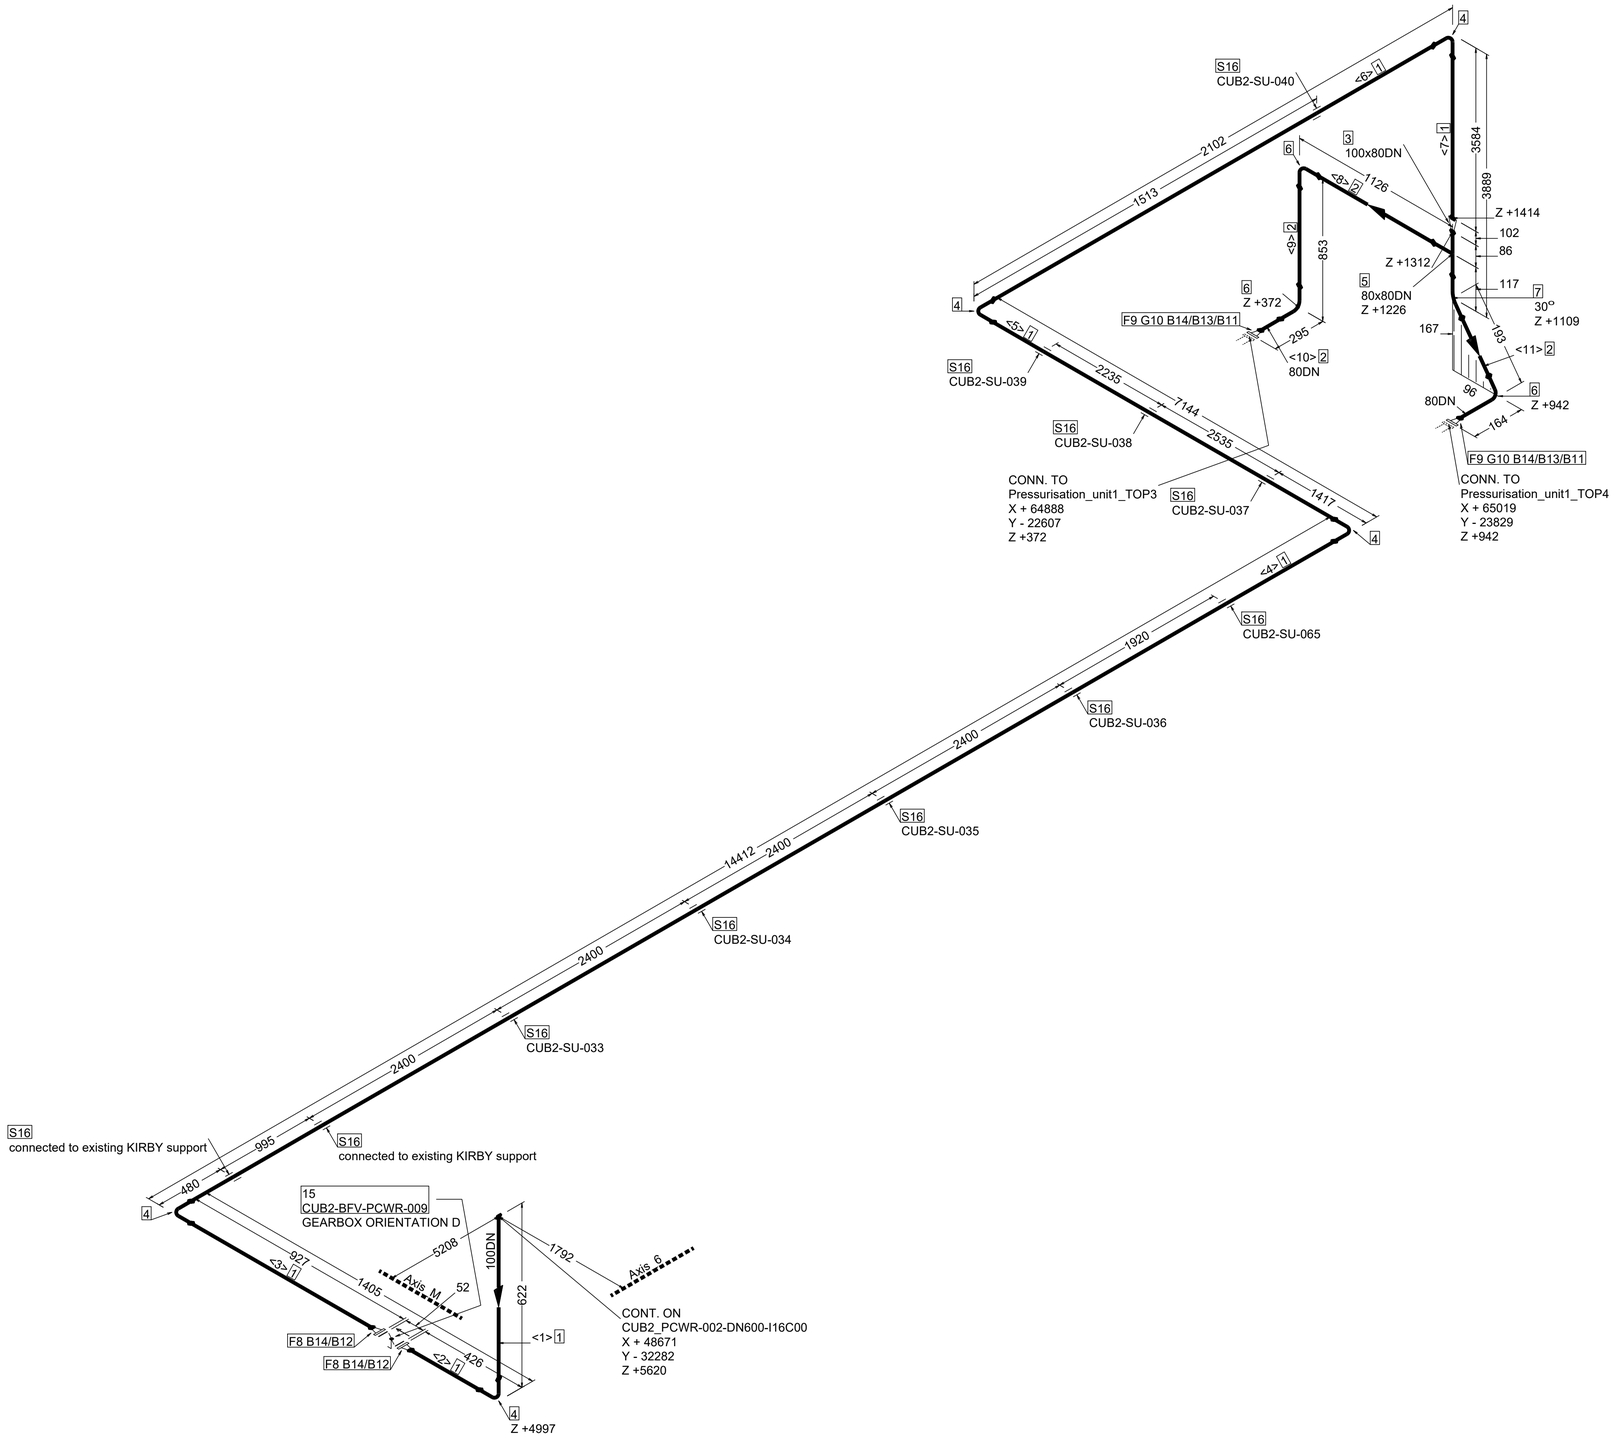

MATERIAL

Pos No.	Description	Material	DN (MM)	Qty.
	PIPE			
1	welded steel pipe - EN 10217-1 - 114.3x3.6 P235GH	P235GH	100	27593MM
2	welded steel pipe - EN 10217-1 - 88.9x3.2 P235GH	P235GH	80	1730MM
	FITTINGS			
3	Reducer concentric - EN 10253-1 - 114.3x3.6/88.9x3.2 P235GH	P235GH	100 x 80	1
4	Elbow - EN 10253-1 - Typ A - Model 3D - 90deg - 114.3x3.6 P235GH	P235GH	100	5
5	Tee - EN10253-1 - Type A - 88.9x3.2/88.9x3.2 P235GH	P235GH	80 x 80	1
6	Elbow - EN 10253-1 - Typ A - Model 3D - 90deg - 88.9x3.2 P235GH	P235GH	80	3
7	Elbow - EN 10253-1 - Typ A - Model 3D - 45deg - 88.9x3.2 P235GH	P235GH	80	1
	FLANGES			
8	Welding Neck Flange, EN1092-1/11/B1, PN16, DN100 P245GH	P245GH	100	2
9	Welding Neck Flange, EN1092-1/11/B1, PN16, DN80 P245GH	P245GH	80	2

MATERIAL

Pos No.	Description	Material	DN (MM)	Qty.
	GASKETS			
10	Flat sealing EN1514-1, Form IBC, PN16, 2mm - DN80 Klingersil C-4400	Klingersil C-4400	80	2
	BOLTS			
11	Hexagon Screw BS4190 - M16 x 70 - 8.8		16	16
12	Hexagon Screw BS4190 - M16 x 40 - 8.8		16	16
13	Hexagon Nut BS4190 - M16 - 8		16	16
14	Washer BS4190 - M16 - Steel zinced		16	48
	VALVES / IN-LINE ITEMS			
15	Butterfly valve - Flowcon - fully lugged - handlever - PN16 - DN100		100	1
	SUPPORTS			
16	ASSEMBLY GROUP BG92-MS41-M10-100-0, DN100+0mm Insul.		100	11

CUT PIPE LENGTH

PIECE NO	CUT LENGTH	DN (MM)	REMARKS	PIECE NO	CUT LENGTH	DN (MM)	REMARKS
<1>	470	100		<2>	222	100	
<3>	723	100		<4>	14108	100	
<5>	6840	100		<6>	1798	100	
<7>	3432	100		<8>	926	80	
<9>	625	80		<10>	131	80	
<11>	48	80					

Insulation Specification:

Pipe Number: CUB2_PCWR-008-DN100-I16C00

Specification: I16C00

Medium:

Pipe data, Inspection Instruction see Pipelist:

X ... Part-No.	X ... Support No.
SPLx ... Spool-No.	... Field weld (FW)
X ... Joint No.	... Shop weld (SW)

Fabricationtolerances acc. EN-ISO-13920

Limits for		
Longitudinal dimensions	Angular dimensions	Straightness-, Flatness- and Parallelismtolerances
Toleranceclass A	Toleranceclass A	Toleranceclass E

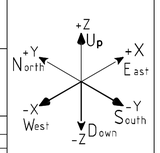

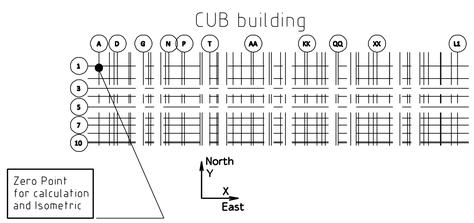

PROTECTION MARK DIN ISO 16016

Rev.	date	drawn	checked	approved	description
1	2020-03-23	Kopacka	Wagner		drawing update

ZAUNER ANLAGENTECHNIK
Zauner Anlagentechnik GmbH
A-4702 Wallern
Mauer 20 / Gewerbepark

FLUOR®
Fluor Consultants B.V,
sivuliike Suomessa
FI-00181 Helsinki
Porkkalankatu 24

project : LPP 5A - K007 - Mechanical & Piping

drawing title : Piping Isometric

CUB2_PCWR-008-DN100-I16C00

Sheet no. 1/1

Revision 1

CAD-NR.:

IERS F.:

IERS D.:

A1

cad system: PDMS / E3D