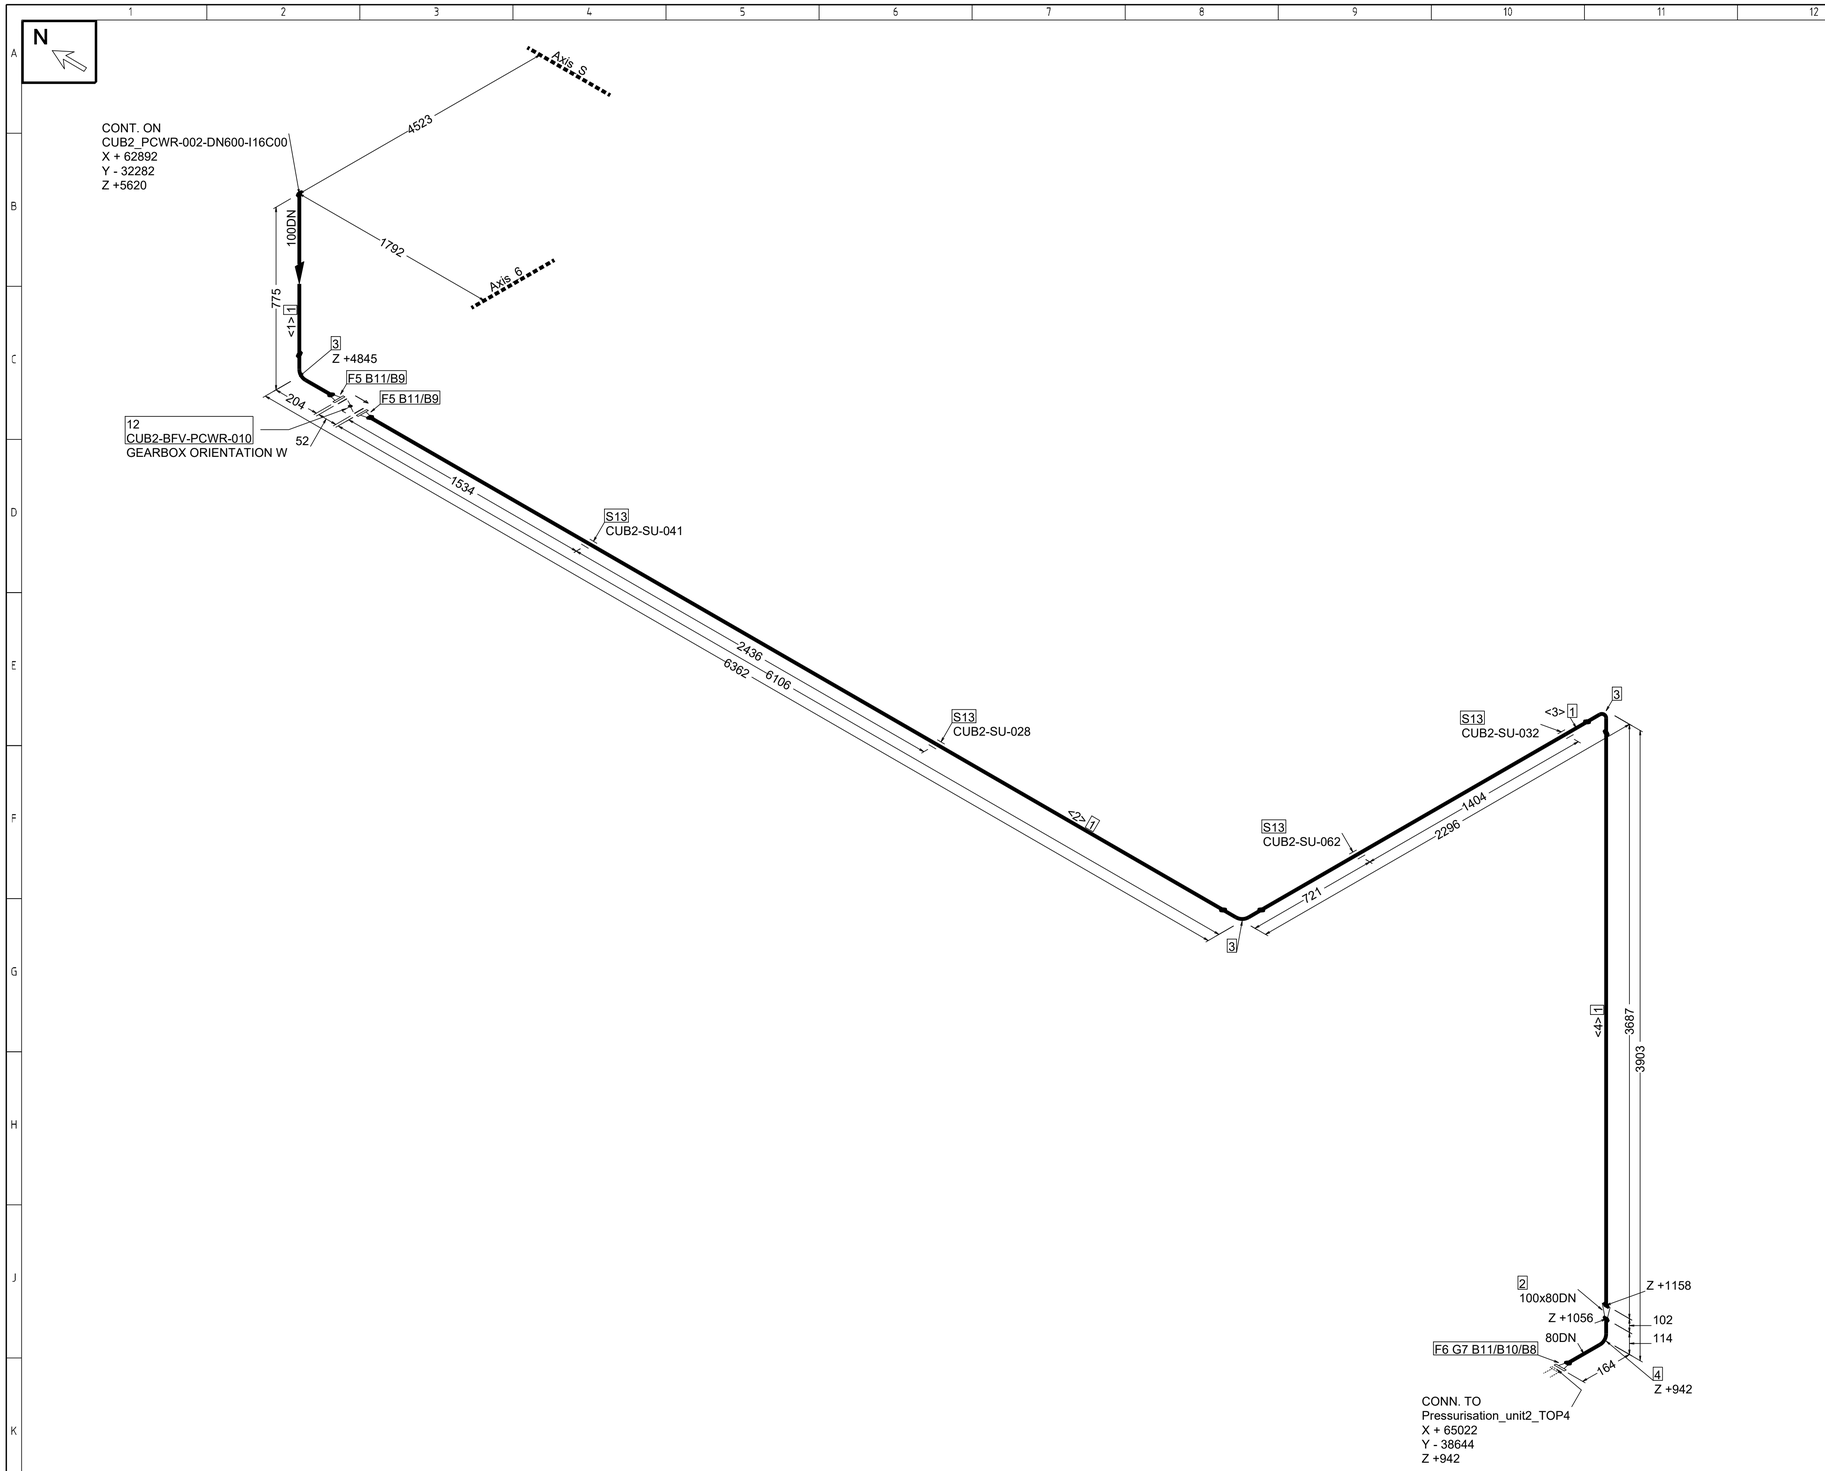

MATERIAL

Pos No.	Description	Material	DN (MM)	Qty.
	PIPE			
1	welded steel pipe - EN 10217-1 - 114.3x3.6 P235GH	P235GH	100	12052MM
	FITTINGS			
2	Reducer concentric - EN 10253-1 - 114.3x3.6/88.9x3.2 P235GH	P235GH	100 x 80	1
3	Elbow - EN 10253-1 - Typ A - Model 3D - 90deg - 114.3x3.6 P235GH	P235GH	100	3
4	Elbow - EN 10253-1 - Typ A - Model 3D - 90deg - 88.9x3.2 P235GH	P235GH	80	1
	FLANGES			
5	Welding Neck Flange, EN1092-1/11/B1, PN16, DN100 P245GH	P245GH	100	2
6	Welding Neck Flange, EN1092-1/11/B1, PN16, DN80 P245GH	P245GH	80	1

MATERIAL

Pos No.	Description	Material	DN (MM)	Qty.
	GASKETS			
7	Flat sealing EN1514-1, Form IBC, PN16, 2mm - DN80 Klingersil C-4400	Klingersil C-4400	80	1
	BOLTS			
8	Hexagon Screw BS4190 - M16 x 70 - 8.8		16	8
9	Hexagon Screw BS4190 - M16 x 40 - 8.8		16	16
10	Hexagon Nut BS4190 - M16 - 8		16	8
11	Washer BS4190 - M16 - Steel zinced		16	32
	VALVES / IN-LINE ITEMS			
12	Butterfly valve - Flowcon - fully lugged - handlever - PN16 - DN100		100	1
	SUPPORTS			
13	ASSEMBLY GROUP BG92-MS41-M10-100-0, DN100+0mm Insul.		100	4

CUT PIPE LENGTH

PIECE NO	CUT LENGTH	DN (MM)	REMARKS	PIECE NO	CUT LENGTH	DN (MM)	REMARKS
<1>	623	100		<2>	5902	100	
<3>	1992	100		<4>	3535	100	

Insulation Specification:

Pipe Number: CUB2_PCWR-010-DN100-I16C00

Specification: I16C00

Medium:

Pipe data, Inspection Instruction see Pipelist:

X...	Part-No.	X..	Support No.
SPLX..	Spool-No.		... Field weld (FW)
X...	Joint No.		... Shop weld (SW)

Fabricationtolerances acc. EN-ISO-13920

Limits for		
Longitudinal dimensions	Angular dimensions	Straightness-, Flatness- and Paralleismtolerances
Toleranceclass A	Toleranceclass A	Toleranceclass E

+Z Up, +Y North, +X East, -X West, -Y South, -Z Down

CUB building

Zero Point for calculation and Isometric

North Y, X East

PROTECTION MARK DIN ISO 16016

Rev.	date	drawn	checked	approved	description
1	2020-03-23	Kopacka	Wagner		drawing update

ZAUNER ANLAGENTECHNIK
Zauner Anlagentechnik GmbH
A-4702 Wallern
Mauer 20 / Gewerbepark

FLUOR®
Fluor Consultants B.V,
sivuliike Suomessa
FI-00181 Helsinki
Porkkalankatu 24

project : LPP 5A - K007 - Mechanical & Piping

drawing title : Piping Isometric

CUB2_PCWR-010-DN100-I16C00

Sheet no. 1/1

Revision 1

CAD-NR :

(ERS.F.:)

(ERS.D.:)

A1

cad system PDMS / E3D