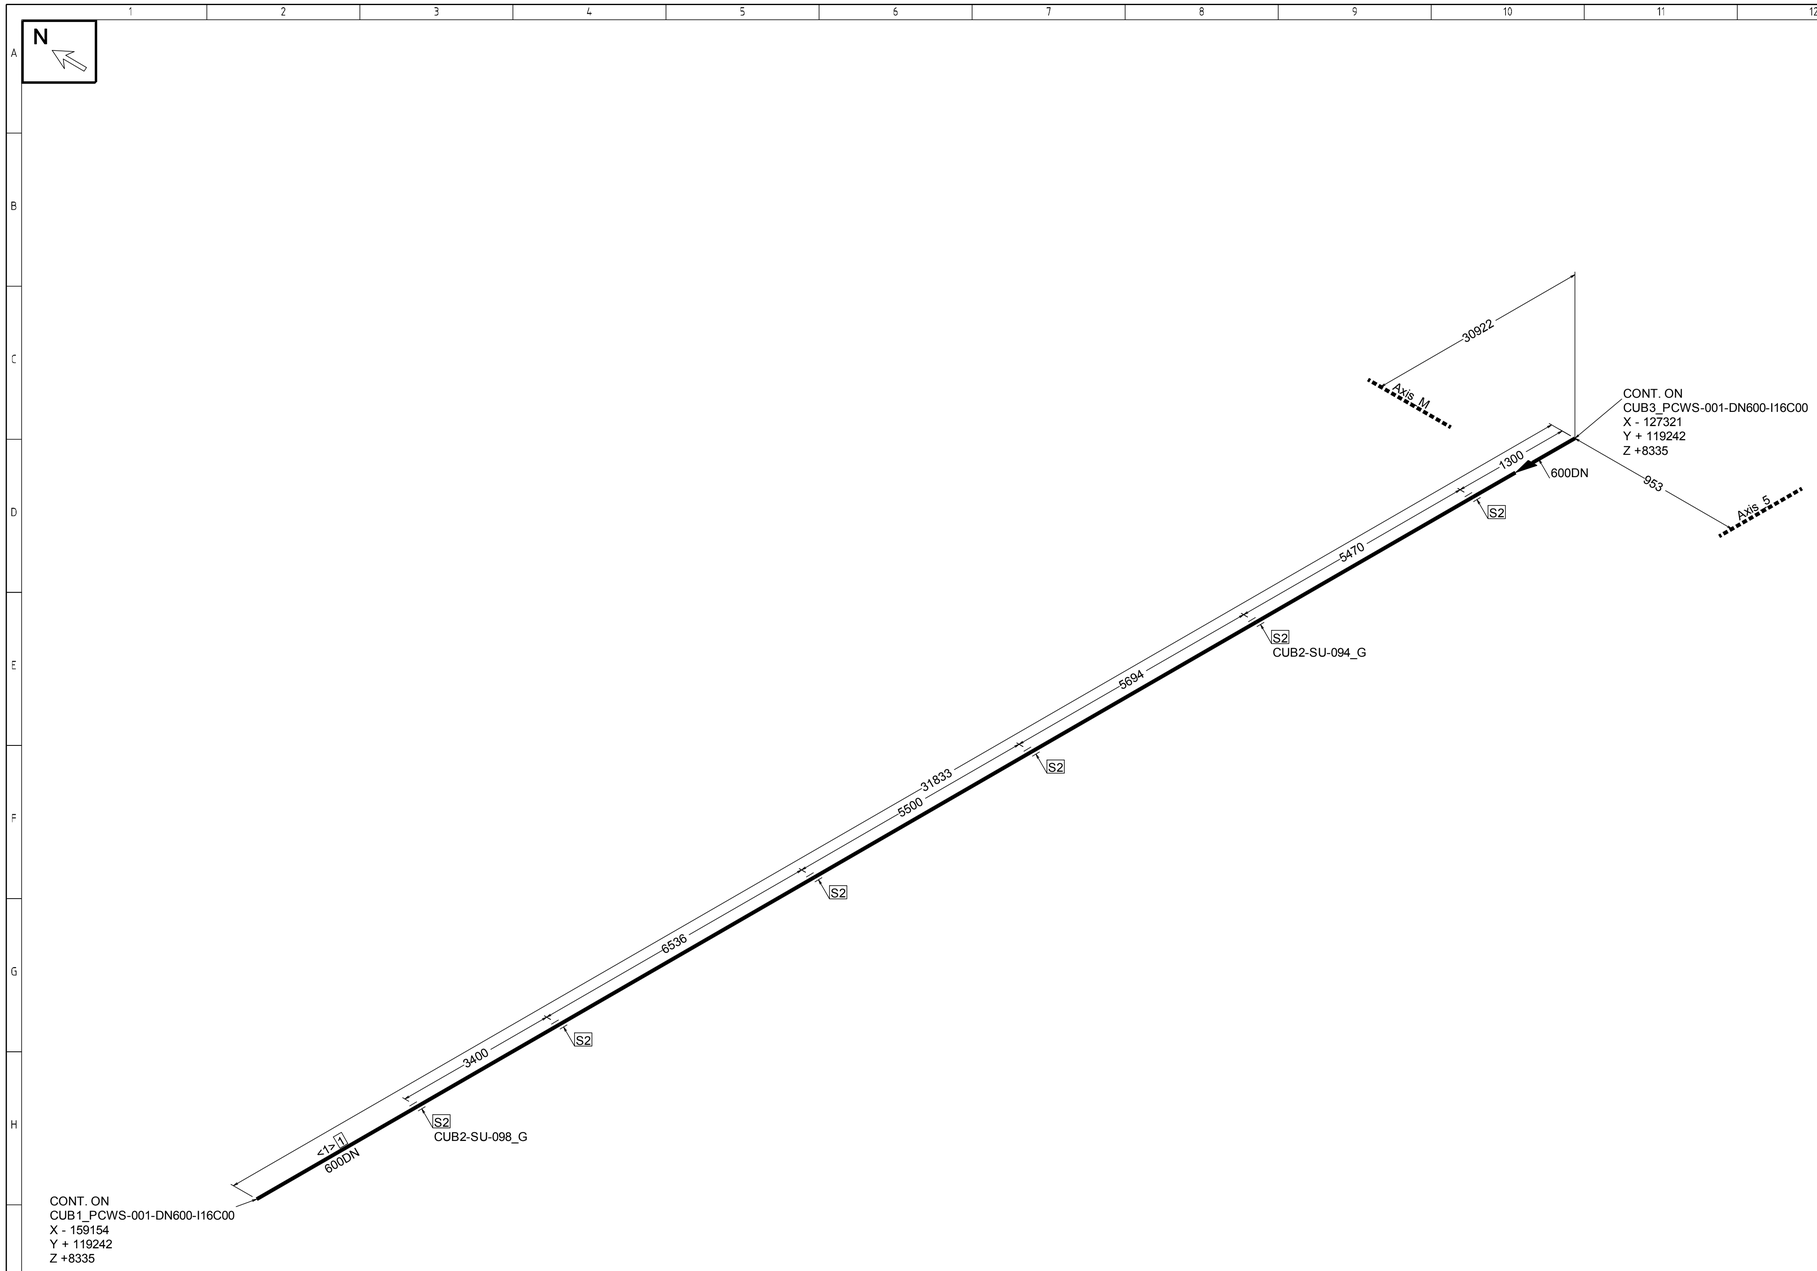

MATERIAL

Pos No.	Description	Material	DN (MM)	Qty.
	PIPE			
1	welded steel pipe - EN 10217-1 - 610x6.3 P235GH	P235GH	600	31833MM

MATERIAL

Pos No.	Description	Material	DN (MM)	Qty.
	SUPPORTS			
2	SLIDING SUPPORT LD-HV090-DN600; ARTICLE NO. 110101		600	6

CUT PIPE LENGTH

PIECE NO	CUT LENGTH	DN (MM)	REMARKS	PIECE NO	CUT LENGTH	DN (MM)	REMARKS
<1>	31833	600					

Insulation Specification:

Pipe Number: CUB2_PCWS-001-DN600-I16C00

Specification: I16C00

Medium:

Pipe data, Inspection Instruction see Pipelist:

X ... Part-No. | X .. Support No.
SPLx .. Spool-No. | ... Field weld (FW)
X ... Joint No. | ... Shop weld (SW)

Fabricationtolerances acc. EN-ISO-13920

Limits for		
Longitudinal dimensions	Angular dimensions	Straightness-, Flatness- and Parallelismtolerances
Toleranceclass A	Toleranceclass A	Toleranceclass E

+Z Up, +Y North, +X East, -X West, -Y South, -Z Down

DC building

Zero Point for calculation and Isometric

North Y, X East

PROTECTION MARK DIN ISO 16016

Rev.	date	drawn	checked	approved	description
0	2019-12-18	Kopacka	Wagner		first issue

ZAUNER ANLAGENTECHNIK

Zauner Anlagentechnik GmbH
A-4702 Wallern
Mauer 20 / Gewerbepark

FLUOR®

Fluor Consultants B.V,
sivuliike Suomessa
FI-00181 Helsinki
Porkkalankatu 24

project : LPP 5A - K007 - Mechanical & Piping

drawing title : Piping Isometric

CUB2_PCWS-001-DN600-I16C00

Sheet no. 1/1

Revision 0

CAD-NR.: | (ERS F-I) | (ERS D-J)

A1

cad system PDMS / E3D