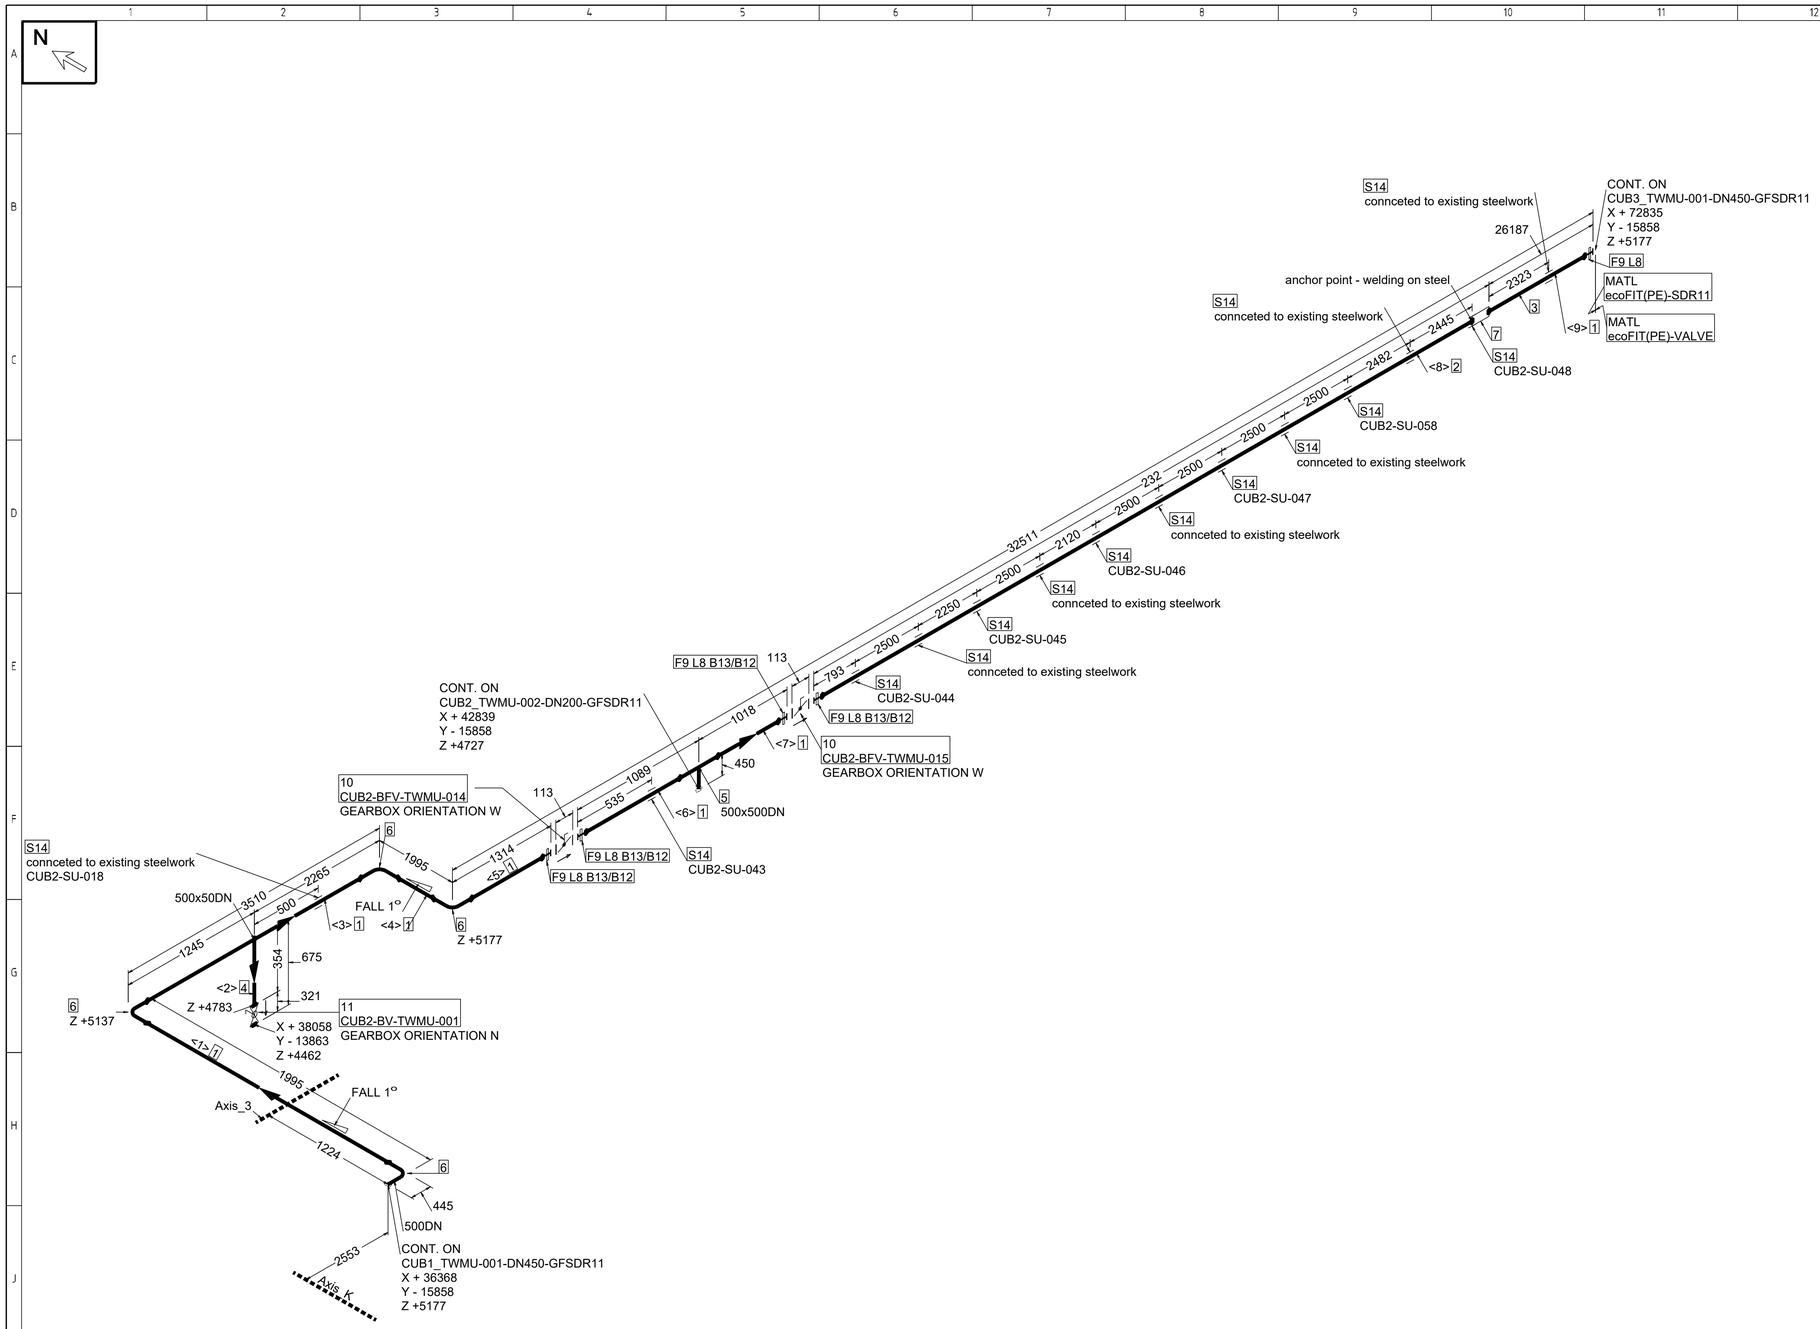

MATERIAL

Pos No.	Description	Material	DN (MM)	Qty.
	PIPE			
1	ecoFIT pipe SDR11 DN500 - 450x40.9 - PN16 PE100	PE100	500	6275MM
2	ecoFIT pipe SDR11 DN500 - 450x40.9 - PN16 PE100	PE100	450	25580MM
3	ecoFIT pipe SDR17.6 DN500 - 450x25.5 - PN10 PE100	PE100	450	2323MM
4	ecoFIT pipe SDR11 DN50 - 63x5.8 - PN16 PE100	PE100	50	102MM
	FITTINGS			
5	ecoFIT tee 90° equal SDR11 DN500 - DN500 - 450x40.9 - 450x40.9 PE100	PE100	500 x 500	1
6	ecoFIT bend 90° SDR11 DN500 - 450x40.9 PE100	PE100	500	4
7	ecoFIT fixed point fitting SDR17.6 DN500 - 450x26.7 PE100	PE100	500	1
	FLANGES			
8	ecoFIT adaptor for butterfly valves SDR11 DN500 - 450x40.9 PE100	PE100	500	5
9	Profiled Backing Flange, PP-Steel For butt fusion systems metric, DN450 - 450x0 PP-STEEL	PP-STEEL	450	5
	VALVES / IN-LINE ITEMS			
10	Metal-Butterfly valve type 038 reduction gear with handwheel ANSI DN350-1200 epoxy FPM DN450 - 450 - PN10		450	2
11	Ball Valve 546, BF spigots long PE100 SDR11, EPDM DN50 - 63x5.8 - PN10 PE100	PE100	50	1

MATERIAL

Pos No.	Description	Material	DN (MM)	Qty.
	BOLTS			
12	Hexagon Screw BS4190 - M27 x 200 - 8.8		27	80
13	Washer BS4190 - M27 - Steel zinced		27	80
	SUPPORTS			
14	SLIDING SUPPORT LD-HV 90 DN 450; ARTICLE NO. K115894		450	14

CUT PIPE LENGTH

PIECE NO	CUT LENGTH	DN (MM)	REMARKS	PIECE NO	CUT LENGTH	DN (MM)	REMARKS
<1>	1105	500		<2>	102	50	
<3>	2620	500	SETON TEE	<4>	1105	500	
<5>	597	500		<6>	367	500	
<7>	296	500		<8>	24818	450	
<9>	3270	500					

Insulation Specification:

Pipe Number: CUB2_TWMU-001-DN450-GFSDR11

Specification: ecoFIT(PE)-SDR11

Medium:

Pipe data, Inspection Instruction see Pipelist:

X ... Part-No.	X .. Support No.
SPLx .. Spool-No.	... Field weld (FW)
X ... Joint No.	... Shop weld (SW)

Fabricationtolerances acc. EN-ISO-13920

Limits for		
Longitudinal dimensions	Angular dimensions	Straightness-, Flatness- and Parallelismtolerances
Toleranceclass A	Toleranceclass A	Toleranceclass E

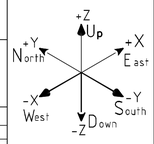

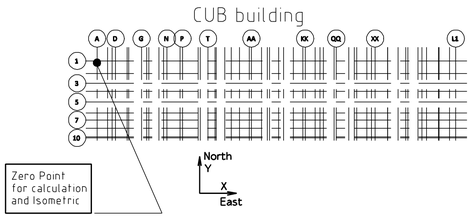

PROTECTION MARK DIN ISO 16016

Rev.	date	drawn	checked	approved	description
0	2020-03-13	Kopacka	Wagner		first issue

ZAUNER ANLAGENTECHNIK

Zauner Anlagentechnik GmbH
A-4702 Wallern
Mauer 20 / Gewerbepark

FLUOR®

Fluor Consultants B.V,
sivuliike Suomessa
FI-00181 Helsinki
Porkkalankatu 24

project : LPP 5A - K007 - Mechanical & Piping

drawing title : Piping Isometric

CUB2_TWMU-001-DN450-GFSDR11

Sheet no. 1/1

Revision 0

CAD-NR :

[ERS.F.I]

[ERS.D.I]

A1

cad system PDMS / E3D