Safety is a primary requirement when working on and off site, the Mechanical Contractor is required to carefully read and understand all safety requirements as a high level safety participation is mandatory.

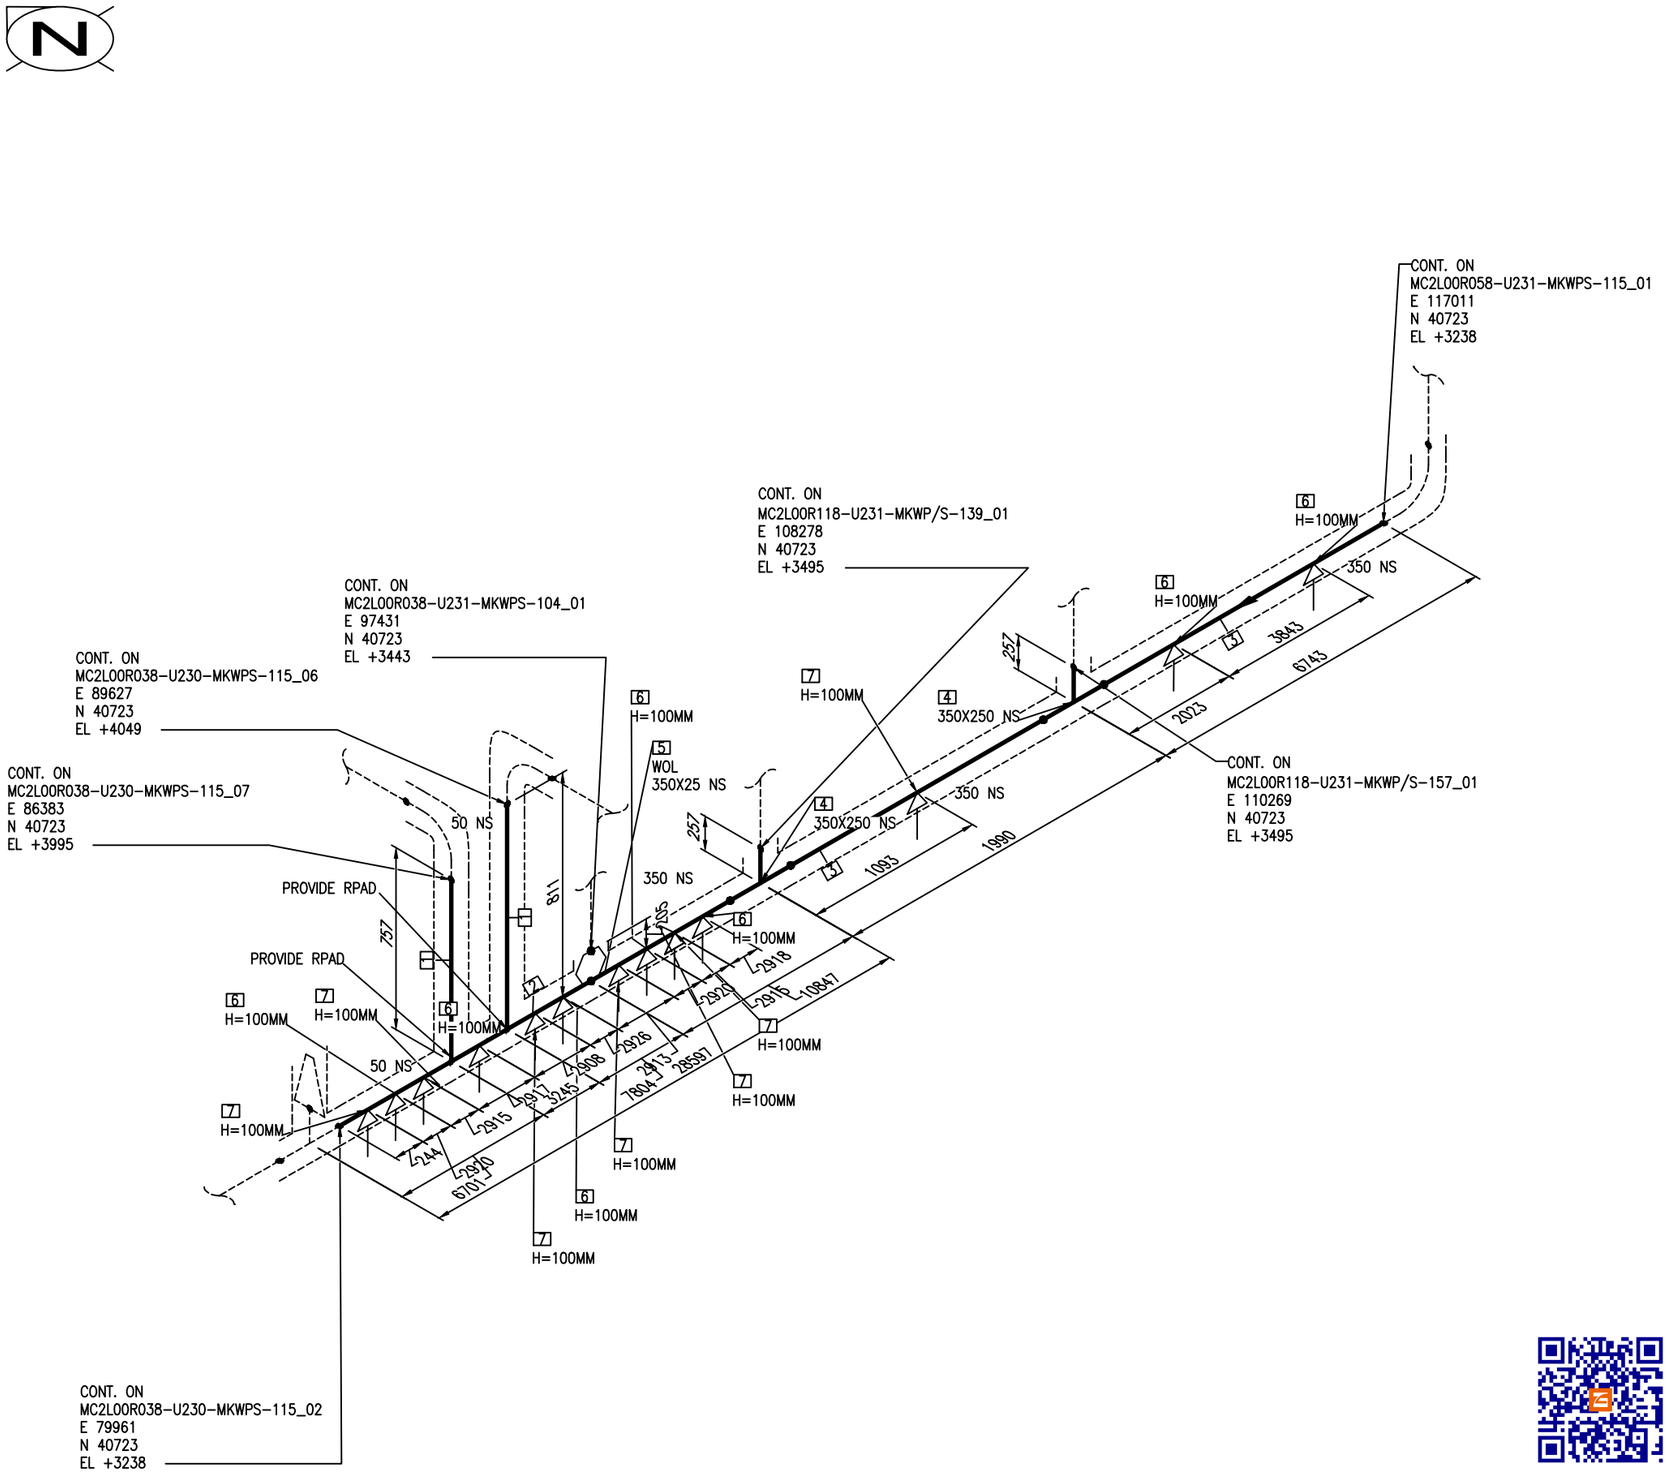

BILL OF MATERIALS

PIPE

ID	DESCRIPTION		SPEC	INSUL	ND	QTY
1	100HF PIPE, EN ISO 1127		LH001	T60	50	1.3M
2	PIPE, EN ISO 1127		LH001	T60	350	28.1M
3	100HF PIPE, EN ISO 1127		LH001	T60	350	7.9M

FITTINGS

ID	DESCRIPTION		SPEC	INSUL	ND	QTY
4	156HF PIPE T-PIECE WITH REDUCING BRANCH, DIN EN 10253-4		LH001	T60	350X250	2

OLETS

ID	DESCRIPTION		SPEC	INSUL	ND	QTY
~~5~~	~~WELDOLET, BW~~		~~LH001~~	~~T60~~	~~350X25~~	~~1~~

PIPE SUPPORTS

ID	DESCRIPTION		SPEC	INSUL	ND	QTY
6	PIPE SUPPORT PS20-04/LD	H=100MM	LH001	T60	350	7
7	PIPE SUPPORT PS20-01/LD	H=100MM	LH001	T60	350	7

[1] DENOTES PIPE SPOOL NO
[1] DENOTES PARTS LIST NO

SHOP WELD | FIELD WELD | SOCKET WELD | SCREWED JOINT | COMPN JOINT | PIPE SUPPORT | LAGGED PIPE | TRACED PIPE

REV	DESCRIPTION	DATE	PIPING	STRESS
0	ISSUED FOR CONSTRUCTION	17-DEC-2021	CB	DD

APPROVALS

NOTES:
1. MECHANICAL CONTRACTOR TO ENSURE ALL PIPEWORK IS ADEQUATELY SUPPORTED.
2. CLOSURE SPOOLS TO BE VERIFIED ON SITE PRIOR TO FABRICATION.
3. ALL WELDS AND JOINTS TO BE CLEAR OF SUPPORT STEELWORK.
4. PIPE SPOOLS AT FFW LOCATIONS TO BE SITE MEASURED PRIOR TO FABRICATION.
5. ALL DIAPHRAGM VALVES ARE TO BE ROTATED TO MANUFACTURERS SPECIFIED DRAIN ANGLES.
6. INSULATION LIMITS FOR PERSONAL PROTECTION TYPE INSULATION WILL BE DETERMINED ON SITE.
7. CONTRACTOR TO LOCATE ALL HIGH POINT VENTS AND LOW POINT DRAINS.
8. CONTRACTOR TO VERIFY EQUIPMENT & INSTRUMENTATION CONNECTIONS AND LOCATIONS PRIOR TO FINAL FABRICATION. & MAKE RELEVANT ADJUSTMENTS TO SUIT.

Jacobs
http://www.jacobs.com/
Mahon Industrial Estate, Blackrock, Cork, Ireland. Tel.: +353 (0)21 4515777 Fax: +353 (0)21 4358977
Merrion House, Merrion Road, Dublin 4, Ireland. Tel.: +353 (0)1 2695666 Fax: +353 (0)1 2695706

CLIENT NAME:	LONZA	JE PROJECT NO:	41AAA4000
PROJECT LOCATION.:	VISP	STRESS CRITICAL:	REF. LINE LIST
PROJECT DESC.:	ORCA	PED CAT:	REF. LINE LIST

DRG.SIZE: A2

DRAWING NO: MC2L00R038-U230-MKWPS-115_01

REV. 0

Safety is a primary requirement when working on and off site, the Mechanical Contractor is required to carefully read and understand all safety requirements as a high level safety participation is mandatory.